ВК-90. Теоретичне креслення (ескізний проєкт, етап 1). Розміри в метрах. Шпація 0,9 м, шпангоути рахуються від транця

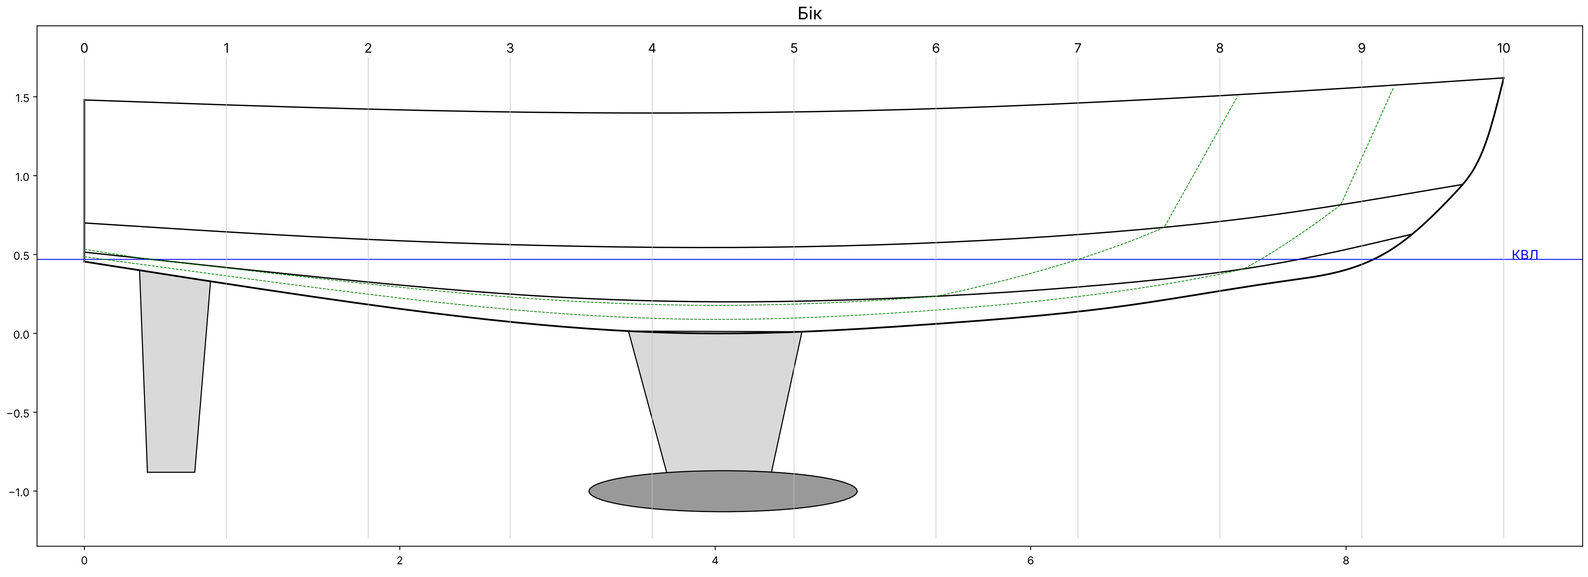

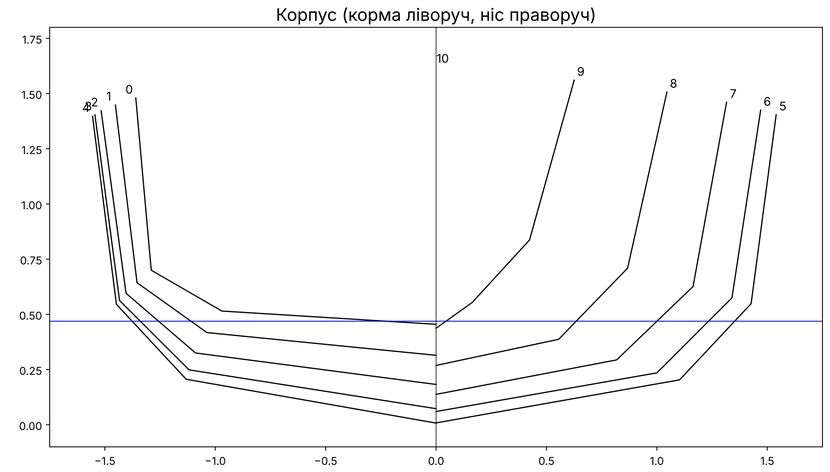

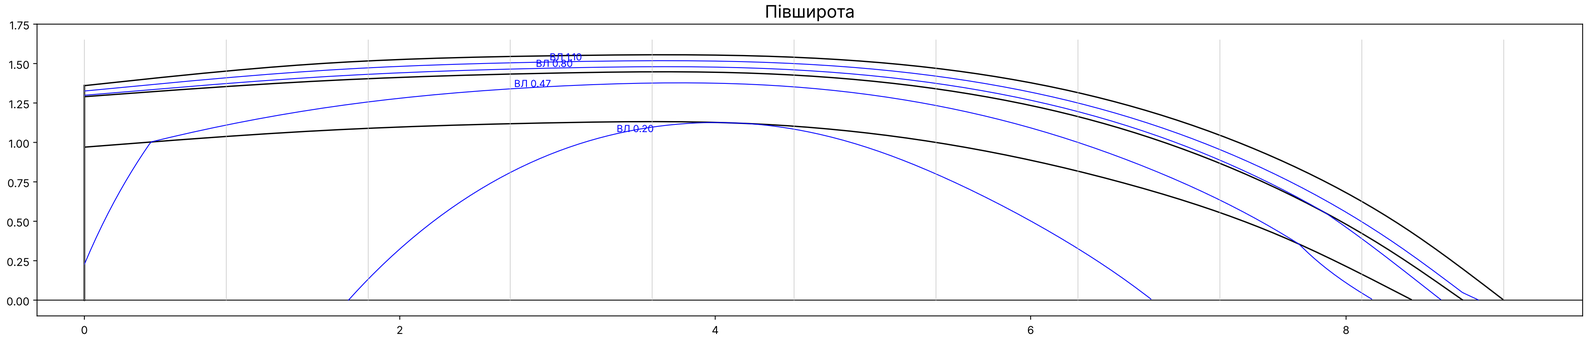

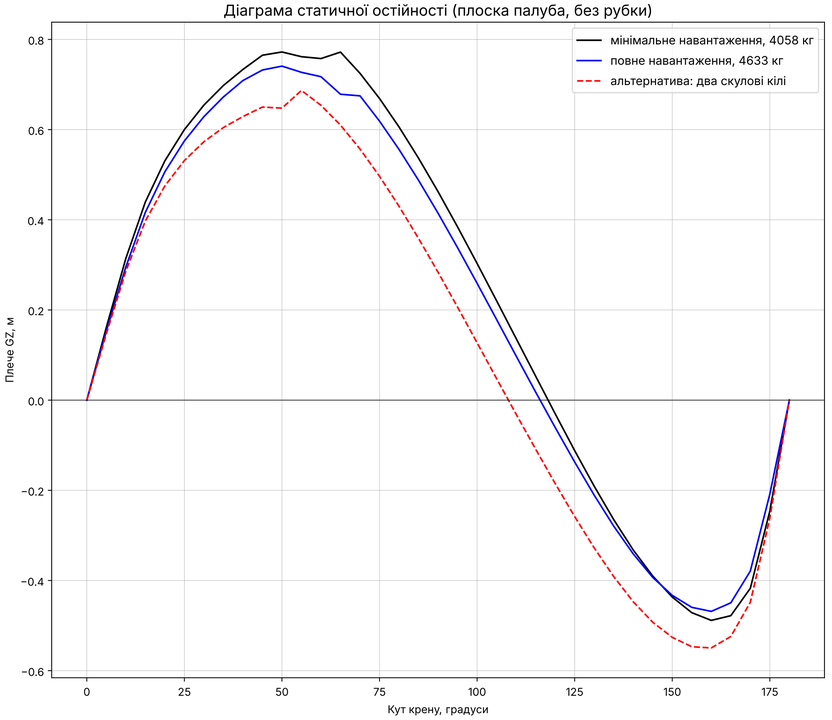

Довжина корпусу 9.00 м Найбільша ширина 3.11 м Довжина по КВЛ 8.15 м Ширина по КВЛ 2.76 м Осадка 1.60 м Водотоннажність на КВЛ 4350 кг

Документ ВК90-001, ревізія 0. Статус: ескіз для погодження, не для виробництва. Зелений пунктир: батокси 0,5 і 1,0 м. Сині лінії: ватерлінії.